

INSPIRAÇÕES DE DESENHO ARQUITETÔNICO BRASIL E MUNDO

POR Luiza Hafner

O QUE É O DESENHO ARQUITETÔNICO

Desenho arquitetônico é uma especialização dentro do desenho técnico voltada para a execução e representação de projetos de arquitetura. Esses registros são feitos por arquitetos ou projetistas e têm como objetivo padronizar e orientar a execução de projetos.

HISTÓRIA DO DESENHO ARQUITETÔNICO

O desenho arquitetônico começou a ser usado a partir do Renascimento. Apesar disso, ainda não havia conhecimentos sistematizados sobre geometria descritiva, o que tornava o processo mais livre e sem normatização.

Foi a partir da Revolução Industrial, com os primeiros projetos de máquinas, que houve a necessidade de criar normatizações para criar processos mais precisos e seguros.

ELEMENTOS UTILIZADOS NO DESENHO ARQUITETÔNICO

Quando falamos de desenho arquitetônico, estamos falando essencialmente do uso de padrões de linha, traços, curvas, círculos, retângulos e símbolos.

É claro que um desenho arquitetônico é muito mais complexo do que isso, mas para começar a entendê-lo o primeiro passo é conhecer seu principal elemento: as linhas

O PRINCIPAL: LINHAS

As linhas são os principais elementos gráficos de um desenho arquitetônico.

São elas que definem o formato, dimensão e posicionamento das paredes, portas, janelas, pilares, vigas, entre outros elementos.

Por esse motivo, as linhas precisam ser representadas de forma legível e com a espessura adequada de acordo com o objetivo da representação.

Veja o que representa cada tipo de traço do desenho arquitetônico:

Traço forte: paredes e elementos estruturais (pilares, vigas, lajes) visíveis no corte de arquitetura

Traço médio: elementos em vista, ou seja, tudo que esteja abaixo (planta baixa) ou além (cortes) do plano de corte, como peitoris, soleiras, mobiliário, ressaltos no piso, vãos de aberturas, paredes em vista, etc. O traço médio também é usado para representar elementos cortados pequenos, como marcos e janelas.

Traço fino: hachuras e texturas que representam elementos de concreto e madeiras. Também é usados para representar os revestimentos de pisos e paredes como pedras e cerâmicas, além de linhas de cotas e chamadas.


O QUE NÃO PODE FALTAR

Perspectivas

A perspectiva ajuda quem está vendo o desenho a ter uma noção de como aquele objeto existe no mundo real.

Ou seja, ela permite enxergar a sua altura, profundidade e largura.


Existem três tipos de perspectivas usadas em desenho técnico: a cavaleira, a cônica e a axonométrica. No desenho arquitetônico, utiliza-se a perspectiva cônica, que também é conhecida como perspectiva do arquiteto.

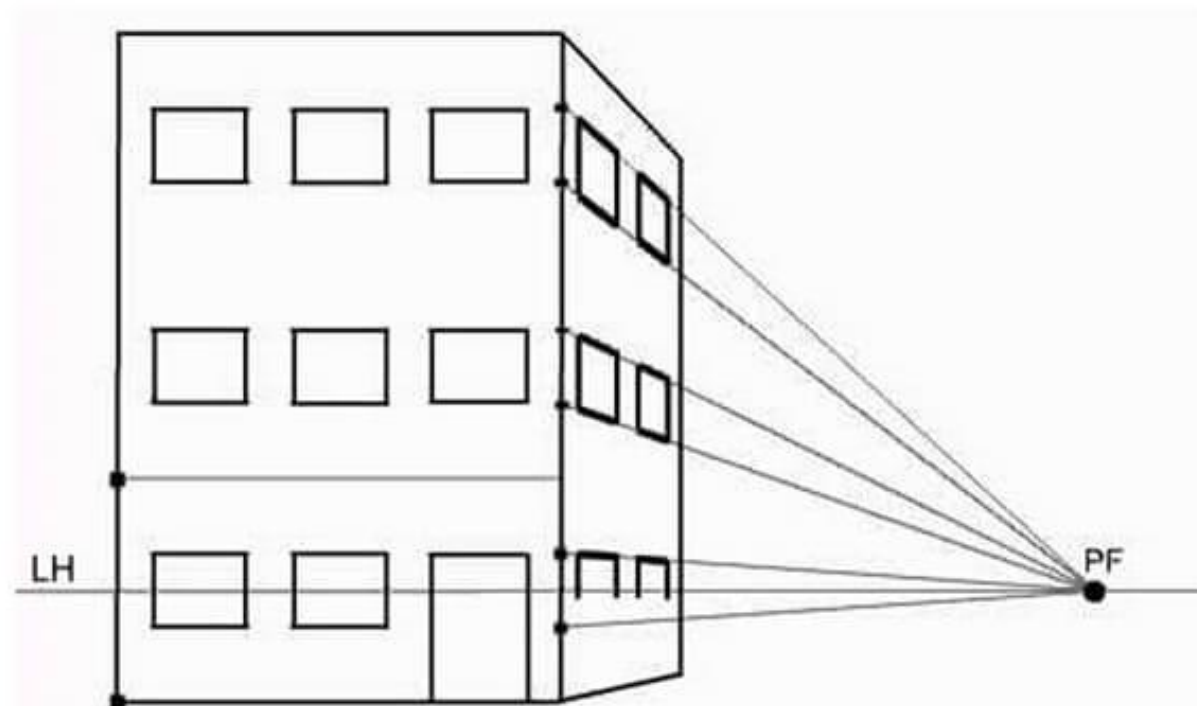

O QUE NÃO PODE FALTAR

Vistas

Vistas, também conhecidas como projeções ortográficas, são formas de representar objetos tridimensionais em superfícies planas. Existem basicamente 3 tipos de vista: a frontal, a superior e a lateral.

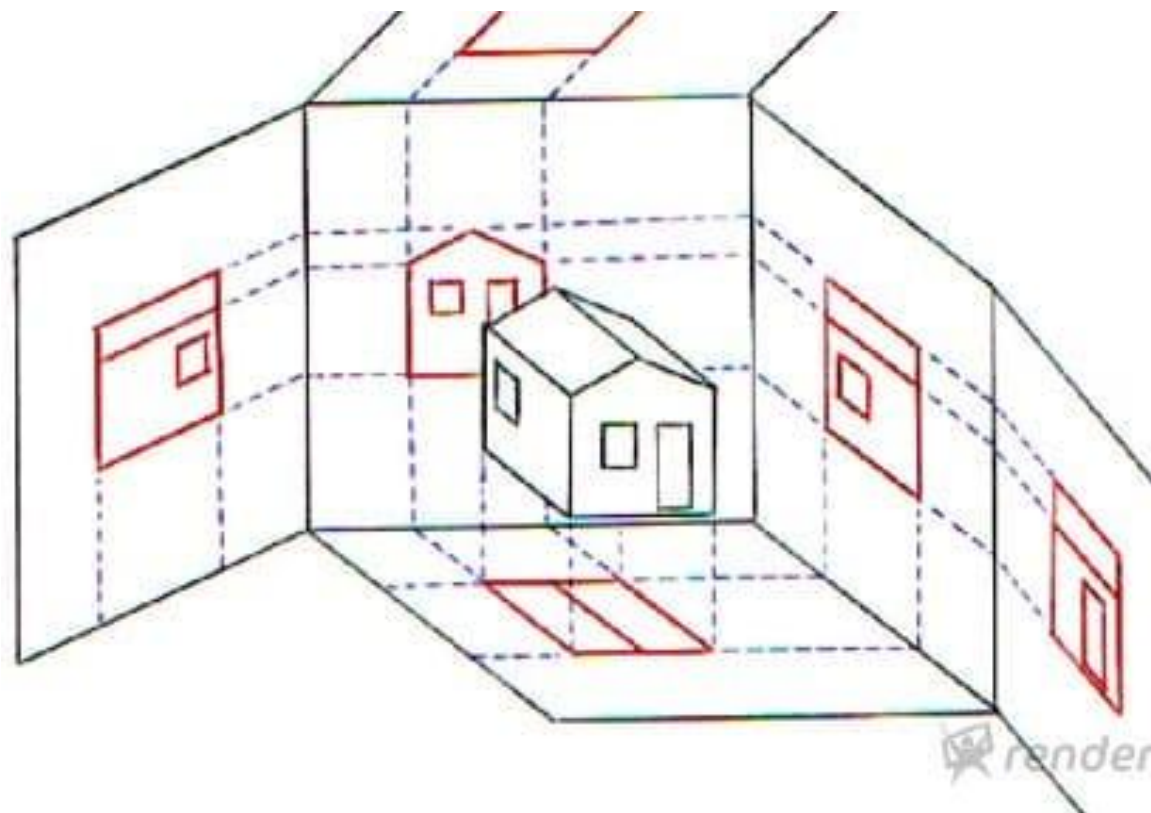

O QUE NÃO PODE FALTAR

Vistas

A escala é uma forma de representar objetos em um plano mantendo as proporções de suas medidas lineares.

As escalas servem para ampliar, reduzir ou manter o tamanho da representação de um objeto em uma planta. Elas indicam a relação do tamanho do desenho com o tamanho real do objeto.

Trata-se de um recurso fundamental no desenho arquitetônico, pois traz as noções reais de um projeto.


CATEGORIA	ESCALAS RECOMENDADAS		
Escala de ampliação	20 : 1	50 : 1	10 : 1
	2 : 1	5 : 1	
Escala natural	1 : 1		
Escala de redução	1 : 2	1 : 5	1 : 10
	1 : 20	1 : 50	1 : 100
	1 : 200	1 : 500	1 : 1 000
	1 : 2 000	1 : 5 000	1 : 10 000

O DESENHO ARQUITETÔNICO E O SURGIMENTO DE BRASÍLIA


A ideia da construção de uma nova capital para o Brasil surgiu durante o governo do presidente Juscelino Kubitschek. Desde o início, já se sabia que ela seria uma cidade grandiosa. Através da criatividade de Lucio Costa e Oscar Niemeyer – que criou o conceito de arquitetura como escultura – ergueu-se uma das maiores criações artísticas da história. Brasília é, hoje, considerada pela UNESCO como Patrimônio da Humanidade.

Através dos croquis desenvolvidos por esses dois grandes arquitetos é possível acompanhar, passo a passo, a evolução das ideias envolvendo o surgimento da nova Capital Federal.


OS CROQUIS DE BRASÍLIA POR LÚCIO COSTA

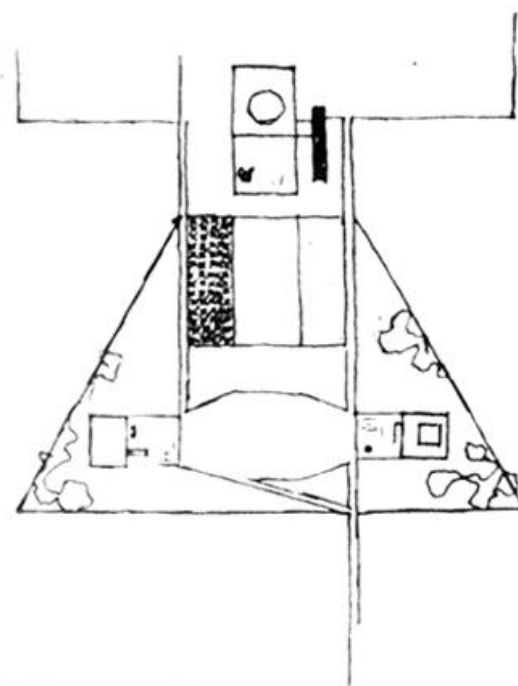


SETOR RESIDENCIAL

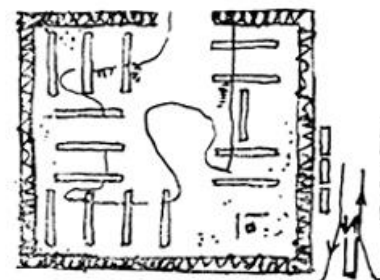

SETOR DOS MINISTÉRIOS

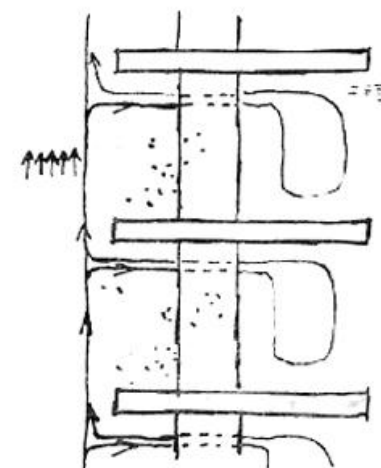

FÓRUM DE PALMEIRAS VERDEJAS
PROPOSTO EM 1936 POR LE CORBUSIER

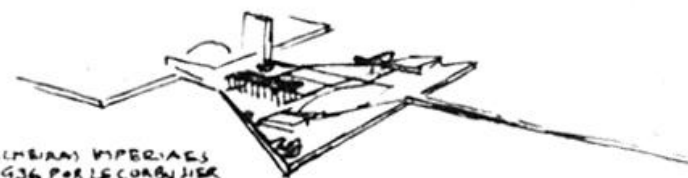


OS CROQUIS DE BRASÍLIA POR LÚCIO COSTA

No final da década de 1950, foi lançado um concurso de projetos para o desenvolvimento do projeto arquitetônico e urbanístico de Brasília. O trabalho escolhido, dentre muitas propostas, foi o de Lúcio Costa. O arquiteto, de nacionalidade francesa, admirava a modernidade brasileira e acreditava na evolução do país.








Essa foi a inspiração para a criação do seu modelo de Plano Piloto, com um traçado em formato de “sinal da cruz”.

PLANO PILOTO

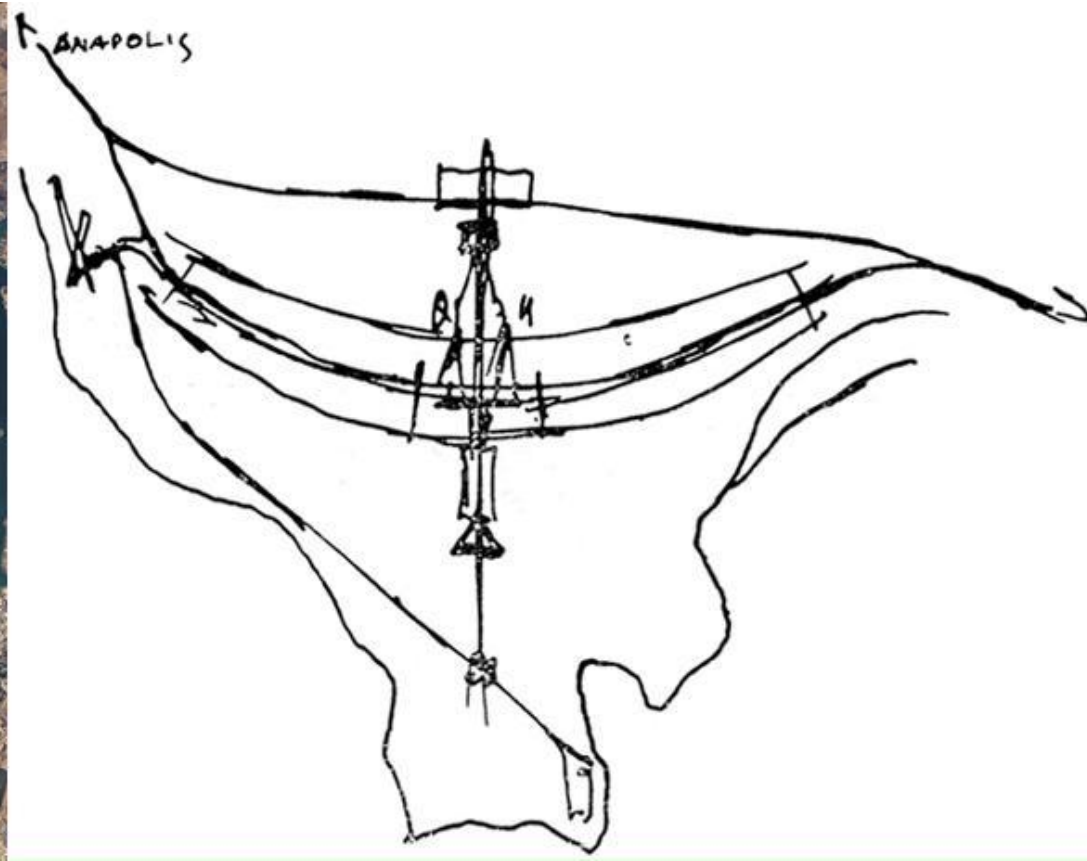


OS CROQUIS DE BRASÍLIA POR OSCAR NIEMEYER


Os projetos criados por Oscar Niemeyer para Brasília são extremamente belos. Eles servem de inspiração para trabalhos de artistas do mundo todo. A principal característica dessas obras é a pureza e a simplicidade dos traços. Suas curvas sutis, quase poéticas, revolucionaram a arquitetura nacional. São exemplos da genialidade desse arquiteto, que explorou novas formas estruturais e materiais em estado bruto, tais como o concreto.

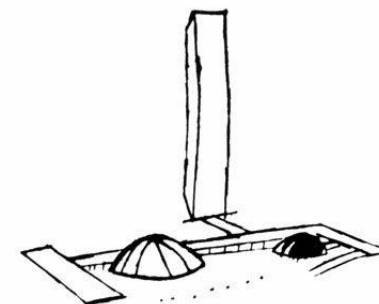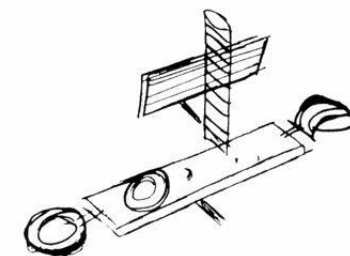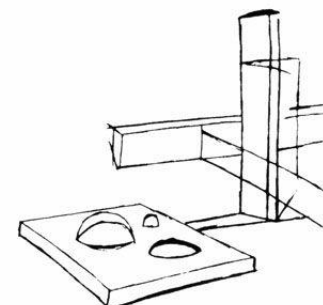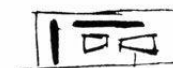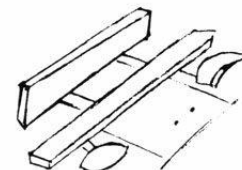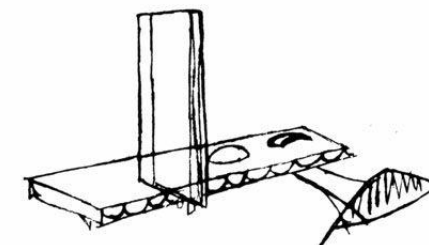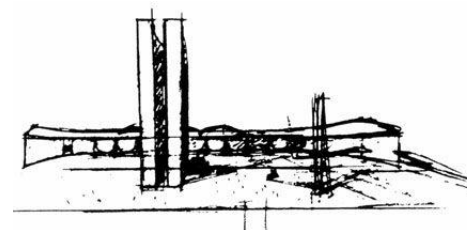

OS CROQUIS DE BRASÍLIA POR OSCAR NIEMEYER

Assim como Lúcio Costa, Niemeyer sempre utilizou os croquis como instrumento de reflexão e busca de soluções arquitetônicas inovadoras. Essa era uma etapa importante para a concepção de seus projetos. Era um meio saudável de extravasar sua inquietação projetual. O momento certo de se entregar às fantasias, de se permitir chegar mais fundo em suas ideias e sentimentos e criar algo único, totalmente espetacular.

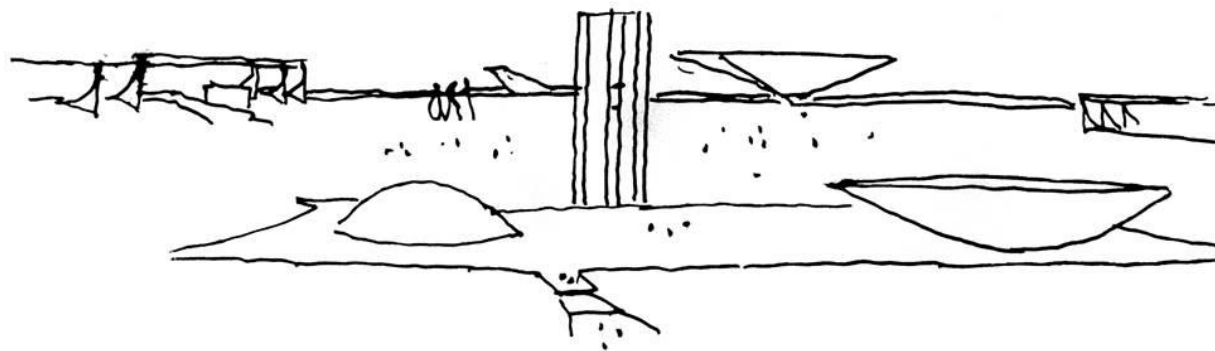

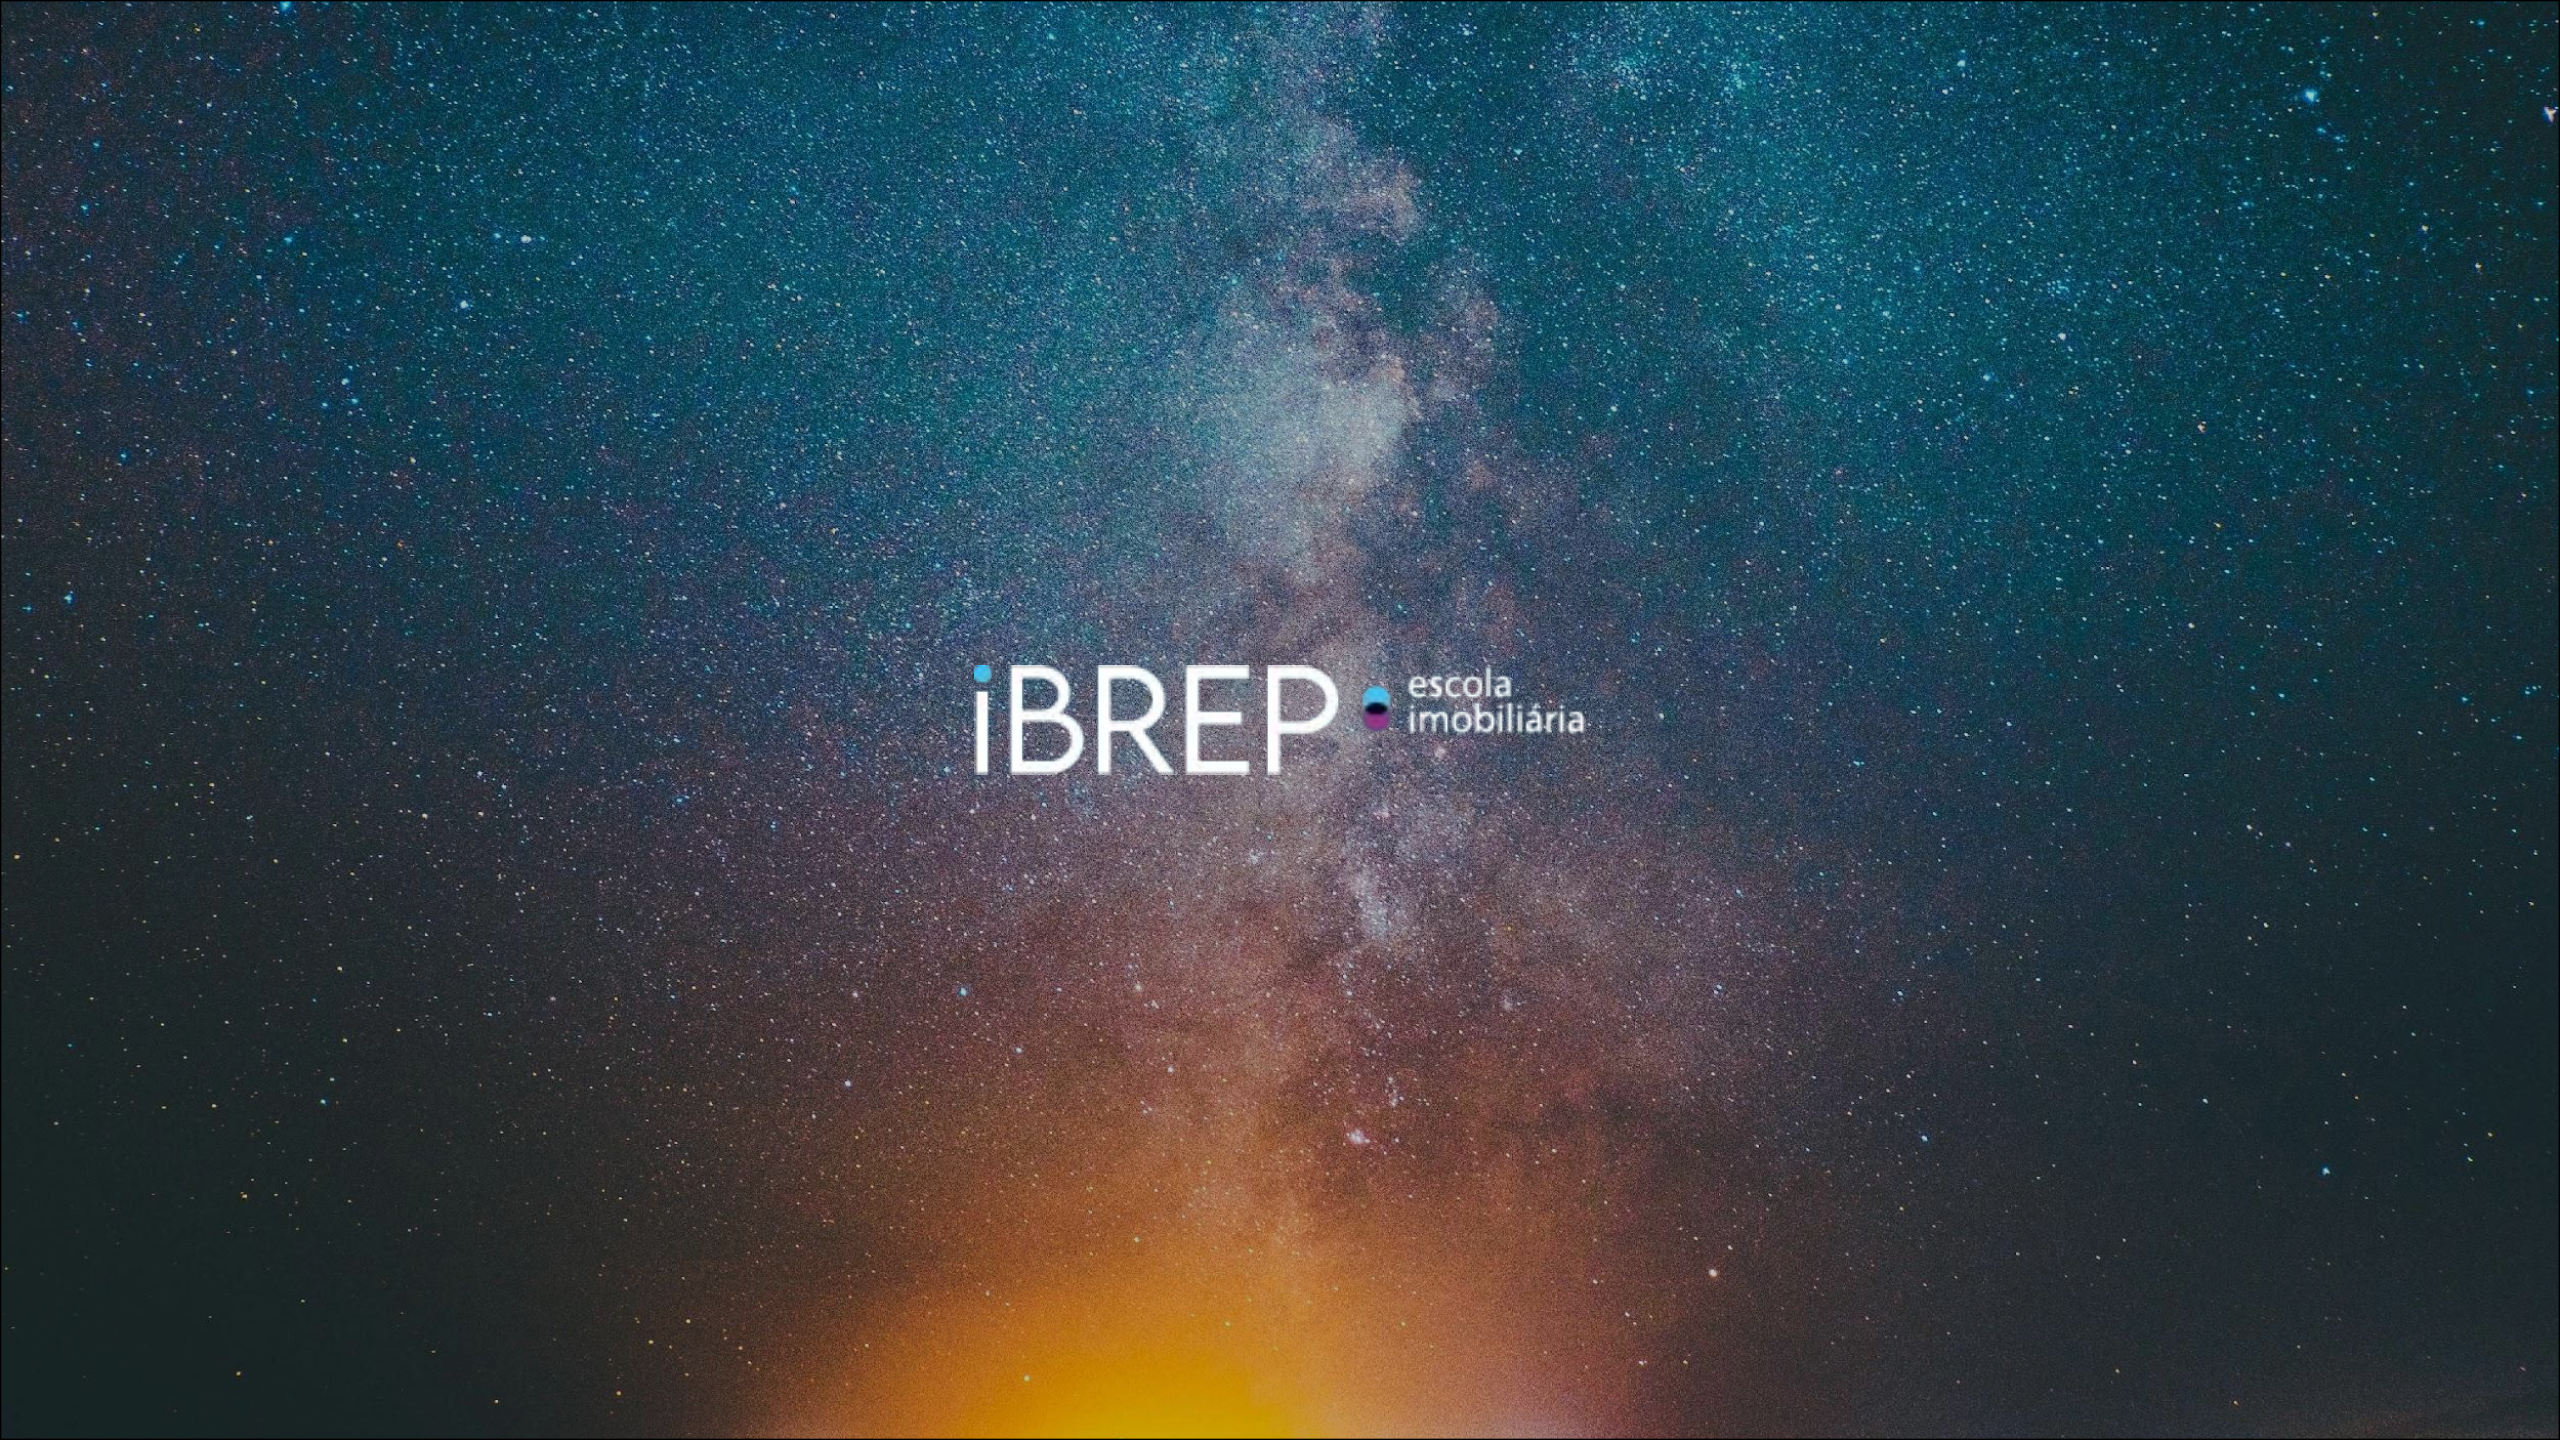The background of the image is a deep space photograph of the Milky Way galaxy, showing a dense band of stars and interstellar dust stretching across the frame. The colors range from dark blues and blacks to warm oranges and yellows near the bottom.

iBREP  escola
imobiliária